LDS HOSPITAL SIMLAB UPDATE

AUDIOVISUAL SHOP DRAWINGS

MARSHALL INDUSTRIES • 3800 WEST 2100 SOUTH, SALT LAKE CITY, UT • 801.266.2428

TABLE OF CONTENTS

REV	DRAWING NUMBER	TITLE	DESCRIPTION	APP BY
AV000 - GENERAL DRAWINGS				
	AV000	TABLE OF CONTENTS		
	AV001	AV LEGENDS AND KEYS	ROUGH-IN	
	AV002	AV LEGENDS AND KEYS	STRUCTURED CABLING	
AV100 - WIREPATH AND BACKBOXES				
	AV101	AUDIOVISUAL SYSTEM	SIM LAB - FLOOR PLAN	
AV200 - REFLECTED CEILING				
	AV201	AUDIOVISUAL SYSTEM	SIM LAB - REFLECTED CEILING PLAN	
AV700 - PLATE DETAILS				
	AV701	SIM LAB	AUDIOVISUAL PLATES	
AV800 - SINGLE LINE DIAGRAMS				
	AV801	CLASSROOM 332	AV SYSTEM FUNCTIONAL	
	AV802	DEBRIEF ROOMS	AV SYSTEM FUNCTIONAL	
	AV803	SIM LABS	AV SYSTEM FUNCTIONAL	
	AV804	APARTMENT 330	AV SYSTEM FUNCTIONAL	
	AV805	WORKROOM 312	AV SYSTEM FUNCTIONAL	
	AV806.1	CONTROL ROOM 328	AV SYSTEM FUNCTIONAL	
	AV806.2	CONTROL ROOM 328	AV SYSTEM FUNCTIONAL	
	AV807	ROOMS 320, 321, AND 322	AV SYSTEM FUNCTIONAL	
	AV808	OR 323	AV SYSTEM FUNCTIONAL	
	AV809	DSP AND SPEAKER ZONES	AV SYSTEM FUNCTIONAL	
AV900 - ENCLOSURE ELEVATIONS				
	AV901	AUDIOVISUAL EQUIPMENT RACK	ERK1.1	

MARSHALL INDUSTRIES

www.marshallind.com

PROJECT INFORMATION

6009

LDS HOSPITAL

SIMLAB UPDATE

CUSTOMER NAME: INTERMOUNTAIN HEALTH	CUSTOMER NUMBER: 10340
SITE NAME: LDS HOSPITAL	SITE NUMBER: 122257

SITE ADDRESS: 8TH AVENUE C STREET, SALT LAKE CITY, UT 84143

SALES PERSON: MATT PRINTY	ENGINEERED BY: MICHAEL PLATTNER
DRAFTER: AARON SMITH	PROJECT MANAGER: DUSTIN DAVIS

DRAWING SET INFORMATION

PHASE: CONSTRUCTION

PUBLISH DATE: 3/17/2026

PLOT SIZE: ARCH FULL BLEED E (36.00 X 48.00 INCHES)

PLOT SCALE: 1' = 1'-0"

APPROVED BY: ----

SHEET REVISION INFORMATION

REVISION: ----

REVISION DATE: ----

REVISION DESCRIPTION: ----

REVISION & ISSUE HISTORY

ISSUED FOR:	REV.	DATE:
---	---	---
---	---	---
LDS HOSPITAL

GENERAL DRAWINGS

TABLE OF CONTENTS

AV000

FILE NAME: AV000.DWG

ENCLOSURE LEGEND

SYM	DESCRIPTION	ELEVATION	QTY 1G	2G	3G	4G	5G	6G
COMMONLY USED WALL BOXES								
C#	GENERIC 3" DEEP BACKBOX. REFER TO # FOR GANG SIZE.	COUNTER HEIGHT	0	0	0	0	0	0
R#		RECEPTACLE HEIGHT	0	0	0	0	0	0
S#		SWITCH HEIGHT	0	0	0	0	0	0

SYM	TYPE	GANG	DESCRIPTION	ELEVATION	QTY
PROJECT SPECIFIC WALL BOXES					
A		1	EXISTING 1G BOX	IN CABINET	1
B		2	EXISTING 2G BOX	IN CABINET	1
D			EXISTING DISPLAY LOCATION	VIF	5
E		2	EXISTING 2G BOX	RECEPTACLE HEIGHT	2
F		1	1G CUT-IN RING	NEAR EXISTING AV PLATE	5
G		1	1G CUT-IN RING	BEHIND EXISTING DISPLAY	5
H		3	EXISTING 3G AV PLATE	RECEPTACLE HEIGHT	5
I					
J					
K					
L					
M					
N					
O					
P					
Q					
T					
U					
V					
W					
X					

SYM	TYPE	GANG	DESCRIPTION	ELEVATION	QTY
CEILING BOXES					
A			EXISTING CEILING SPEAKER	FLUSH IN CEILING	5
B			EXISTING CEILING BUTTON MIC	FLUSH IN CEILING	23
C			FLUSH PTZ CEILING CAMERA	ON CEILING	26
D					
E					
F					
G					
H					
I					
J					
K					
L					
M					

SYM	TYPE	GANG	DESCRIPTION	ELEVATION	QTY
TABLE BOXES					
A					
B					
C					
D					
E					
F					
G					
H					
I					
J					
K					
L					

SYM	TYPE	GANG	DESCRIPTION	ELEVATION	QTY
FLOOR BOXES					
A					0
B					
C					
D					
E					
F					
G					
H					
I					
J					
K					
L					
M					

SYM	TYPE	GANG	DESCRIPTION	ELEVATION	QTY
EQUIPMENT RACKS					
A			EXISTING AV EQUIPMENT RACK	ON FLOOR	1
B					
C					
D					
E					
F					
G					
H					
I					
J					
K					
L					

AV100/AV200 WIRE PATH AND ENCLOSURE EXAMPLE

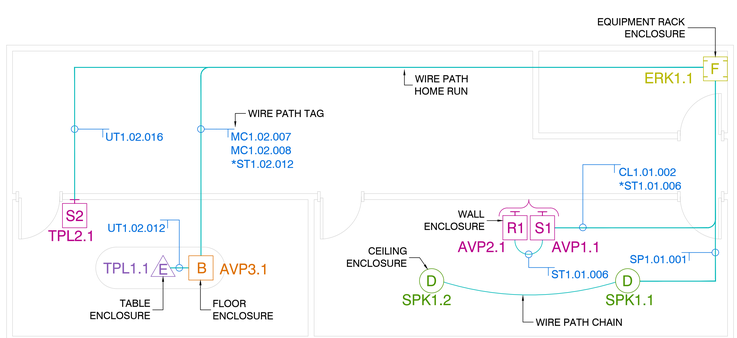

LOCATION EXAMPLE

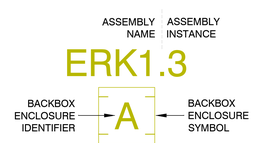

WIRE PATH TAG EXAMPLE

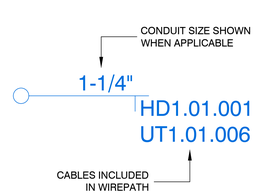

AV300 EQUIPMENT PLACEMENT EXAMPLE

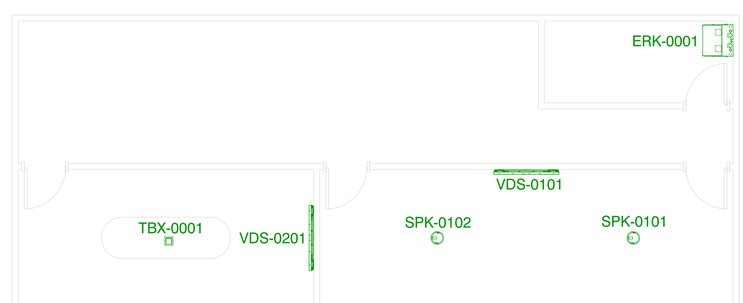

EQUIPMENT BLOCK EXAMPLE

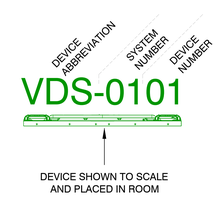

MARSHALL INDUSTRIES

www.marshallind.com

PROJECT INFORMATION

6009

LDS HOSPITAL

SIMLAB UPDATE

CUSTOMER NAME: INTERMOUNTAIN HEALTH	CUSTOMER NUMBER: 10340
SITE NAME: LDS HOSPITAL	SITE NUMBER: 122257
SITE ADDRESS: 8TH AVENUE C STREET SALT LAKE CITY, UT 84143	
SALES PERSON: MATT PRINTY	ENGINEERED BY: MICHAEL PLATTNER
DRAFTER: AARON SMITH	PROJECT MANAGER: DUSTIN DAVIS

DRAWING SET INFORMATION

PHASE: CONSTRUCTION

PUBLISH DATE: 3/17/2026

PLOT SIZE: ARCH FULL BLEED E (36.00 X 48.00 INCHES)

PLOT SCALE: 1' = 1'-0"

APPROVED BY: ----

SHEET REVISION INFORMATION

REVISION: ----

REVISION DATE: ----

REVISION DESCRIPTION: ----

REVISION & ISSUE HISTORY

ISSUED FOR:	REV.	DATE:
---	---	---
---	---	---
LDS HOSPITAL

GENERAL DRAWINGS

AV LEGENDS AND KEYS

ROUGH-IN

AV001

FILE NAME: AV000.DWG

ABRV.	DESCRIPTION
AAP	AMPLIFIED AUDIO PANEL
ACU	ACOUSTIC MATERIAL
ADC	AUDIO CONFERENCING
ALS	ASSISTED LISTENING SYSTEM
AMP	AMPLIFIER
AMS	ASSET MANAGEMENT
ANN	ANNOTATOR
ANT	ANTENNA
ARS	AUDIO RESPONSE SYSTEM
ASP	AUDIO SIGNAL PROCESSOR
AVF	AUDIO/VIDEO FURNITURE
AVL	AUDIO/VIDEO LIFT
AVP	AUDIO/VIDEO PANEL
AVT	AUDIO/VIDEO PANEL
BAG	EQUIPMENT BAG
BGM	BACKGROUND MUSIC SYSTEM
BOB	BREAK OUT BOX
CAM	CAMERA
CBX	CEILING BOX
CCU	CAMERA CONTROL UNIT
CLK	CLOCK
CNT	CONTROLLER
CNV	CONVERTER
COD	ENCODER/DECODER
CPU	COMPUTER
CRD	CARD/MODULE/INSERT
DAR	DIGITAL AUDIO RECORDER
DMP	DIGITAL MEDIA PLAYER
DMR	DIGITAL MEDIA RECORDER
DMT	DIGITAL MEDIA TRANSMISSION
DOC	DOCUMENT CAMERA
DSP	DIGITAL SIGNAGE SYSTEM
DTP	DISTANCE TRANSPORT
DVR	DIGITAL VIDEO RECORDER
DWR	DRAWER
EFX	EFFECTS PROCESSOR
EMI	IR/RF EMITTER
ENC	CHASSIS/CARD ENCLOSURE
ERK	EQUIPMENT RACK
FAN	FAN
FBX	FLOOR BOX
GUI	GRAPHICAL USER INTERFACE
ICS	INTERCOM SYSTEM
IFB	INTERUPTED FOLDBACK
INT	INTERFACE
IWB	WHITE BOARD
KPD	KEYPAD CONTROL
LEN	LENS
LGT	LIGHTING SYSTEM
MDI	MIDI CONTROLLER
MIC	MICROPHONE
MIX	MIXER
MOD	MODULATOR/DEMODULATOR
MON	MONITOR
MSG	MESSAGING SYSTEMS
MSK	SOUND MASKING SYSTEM
MTR	MAGNETIC TAPE RECORDER
NCS	NURSE CALL SYSTEM
NMD	NETWORK MEDIA DEVICE
NVR	NETWORK VIDEO RECORDER
NWD	NETWORK DEVICE
ODR	OPTICAL DISK RECORDER
PAS	PUBLIC ADDRESS SYSTEM
PGS	PAGING SYSTEM

ABRV.	DESCRIPTION
PPL	PATCH PANEL
PRJ	PROJECTOR
PWR	POWER DEVICE
REM	REMOTE CONTROL
RMK	RACK MOUNT KIT
ROB	ROBOTIC SYSTEM
RTS	DISCUSSION SYSTEM
SBX	STAGE BOX/SNAKE
SCN	PROJECTION SCREEN
SCR	SCALER/SCAN CONVERTER
SNS	SENSOR DEVICE
SOF	SOFTWARE
SPK	SPEAKER
SPT	RF SPLITTER
SWT	SWITCHER
TBX	TABLE BOX
TEL	TELEPHONES
TMP	TAPE MEDIA PLAYER
TPL	TOUCH PANEL
TRX	TRANSMITTER/RECIEVER
UPS	UNINTERRUPTABLE POWER SUPPLY
VDC	VIDEO CONFERENCING
VDS	VIDEO DISPLAY
VSP	VIDEO SIGNAL PROCESSOR
VWS	VIDEO WALL SYSTEM
WAP	WIRELESS ACCESS POINT
WBX	WALL BOX
WMR	WIRELESS TX/RX
XDA	DISTRIBUTION AMPLIFIER
XMR	TRANSFORMER
XXX	UNKNOWN

CABLE LEGEND

ID	MAKE	MODEL	DESCRIPTION	PLENUM
CONTROL				
CL1				
CL2				
CL3				
CL4				
CL5				
COAX				
CX1				
CX2				
CX3				
CX4				
CX5				
FIBER OPTIC				
FB1				
FB2				
FB3				
FB4				
HDMI				
HD1			3' HDMI CABLE	
HD2	C2G	CG10377	6' HDMI CABLE	
HD3			10' HDMI CABLE	
HD4			15' HDMI CABLE	
HD5			30' HDMI CABLE	
HD6				
HD7				
HD8				
MICROPHONE OR LINE LEVEL AUDIO				
MC1	WEST PENN	25454BK	MIC/LINE CABLE	X
MC2				
MC3				
MC4				
MC5				
MULTI-FUNCTION				
MF1				
MF2				
MF3				
MF4				
POWER				
PW1				
PW2				
PW3				
PW4				
PW5				
SPECIAL				
SL1				
SL2				
SL3				
SL4				
SPEAKER				
SP1	WEST PENN	25225BGY	16AWG SPEAKER CABLE	X
SP2				
SP3				
SP4				
SP5				
SHIELDED TWISTED PAIR				
ST1				
ST2				
ST3				
ST4				
ST5				
USB				
US1			PREMADE USB CABLE	
US2				
US3				
US4				
US5				
UNSHIELDED TWISTED PAIR				
UT1	WEST PENN	254246EZBK	CAT6 DATA CABLE	X
UT2				
UT3				
UT4				
UT5				

AV800 SINGLE LINE DIAGRAM EXAMPLE

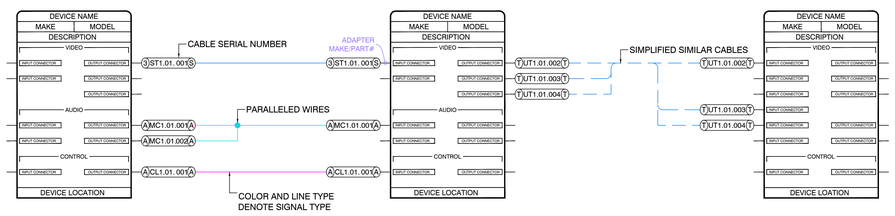

AV800 CABLE SERIAL NUMBER EXAMPLE

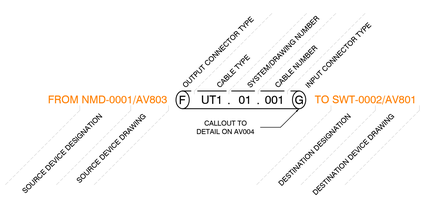

LINE DESIGNATIONS KEY

- BULK - AUDIO
- PATCH - AUDIO
- BULK - VIDEO
- PATCH - VIDEO
- BULK - CONTROL
- PATCH - CONTROL
- BULK - GENERIC
- PATCH - GENERIC

MARSHALL INDUSTRIES

www.marshallind.com

PROJECT INFORMATION

6009

LDS HOSPITAL

SIMLAB UPDATE

CUSTOMER NAME: INTERMOUNTAIN HEALTH	CUSTOMER NUMBER: 10340
SITE NAME: LDS HOSPITAL	SITE NUMBER: 122257
SITE ADDRESS: 8TH AVENUE C STREET SALT LAKE CITY, UT 84143	
SALES PERSON: MATT PRINTY	ENGINEERED BY: MICHAEL PLATTNER
DRAFTER: AARON SMITH	PROJECT MANAGER: DUSTIN DAVIS

DRAWING SET INFORMATION

PHASE: CONSTRUCTION

PUBLISH DATE: 3/17/2026

PLOT SIZE: ARCH FULL BLEED E (36.00 X 48.00 INCHES)

PLOT SCALE: 1' = 1'-0"

APPROVED BY: -----

SHEET REVISION INFORMATION

REVISION: ----

REVISION DATE: -----

REVISION DESCRIPTION: -----

REVISION & ISSUE HISTORY

ISSUED FOR:	REV.	DATE:
---	---	---
---	---	---
LDS HOSPITAL

GENERAL DRAWINGS

AV LEGENDS AND KEYS

STRUCTURED CABLING

AV002

FILE NAME: AV000.DWG

SHEET ENCLOSURE LEGEND

LOCATION	SYM	GANG	DESCRIPTION	ELEVATION
AVP1	E	2	EXISTING 2G BOX	RECEPTACLE HEIGHT
AVP2	F	1	1G CUT-IN RING	NEAR EXISTING AV PLATE
AVP3	H	3	EXISTING 3G AV PLATE	RECEPTACLE HEIGHT
AVP4	H	3	EXISTING 3G AV PLATE	RECEPTACLE HEIGHT
AVP5	B	2	EXISTING 2G BOX	IN CABINET
ERK1	A		EXISTING AV EQUIPMENT RACK	ON FLOOR
TPL1	A	1	EXISTING 1G BOX	IN CABINET
VDS1	D		EXISTING DISPLAY LOCATION	VIF
VDS1	G	1	1G CUT-IN RING	BEHIND EXISTING DISPLAY

SHEET CABLE LEGEND

ABBREV	MAKE	MODEL	DESCRIPTION	QTY
MC1	WEST PENN	25454BK	MIC/LINE CABLE	6
UT1	WEST PENN	254246EZBK	CAT6 DATA CABLE	32

1 **SIM LAB - FLOOR PLAN**
AUDIOVISUAL SYSTEM
SCALE: 1/8" = 1'-0"

MARSHALL INDUSTRIES

www.marshallind.com

PROJECT INFORMATION

6009

LDS HOSPITAL

SIMLAB UPDATE

CUSTOMER NAME: INTERMOUNTAIN HEALTH	CUSTOMER NUMBER: 10340
SITE NAME: LDS HOSPITAL	SITE NUMBER: 122257
SITE ADDRESS: 8TH AVENUE C STREET SALT LAKE CITY, UT 84143	
SALES PERSON: MATT PRINTY	ENGINEERED BY: MICHAEL PLATTNER
DRAFTER: AARON SMITH	PROJECT MANAGER: DUSTIN DAVIS

DRAWING SET INFORMATION

PHASE: CONSTRUCTION

PUBLISH DATE: 3/17/2026

PLOT SIZE: ARCH FULL BLEED E (36.00 X 48.00 INCHES)

PLOT SCALE: 1' = 1'-0"

APPROVED BY: -----

SHEET REVISION INFORMATION

REVISION: ----

REVISION DATE: -----

REVISION DESCRIPTION: -----

REVISION & ISSUE HISTORY

ISSUED FOR:	REV.	DATE:
---	---	---
---	---	---
LDS HOSPITAL

WIREPATH AND BACKBOXES

AUDIOVISUAL SYSTEM

SIM LAB - FLOOR PLAN

AV101

FILE NAME: AV100.DWG

SHEET ENCLOSURE LEGEND

LOCATION	SYM	GANG	DESCRIPTION	ELEVATION
CAM1	C		EXISTING PTZ CEILING CAMERA	ON CEILING
MIC1	B		EXISTING CEILING BUTTON MIC	FLUSH IN CEILING
SPK1	A		EXISTING CEILING SPEAKER	FLUSH IN CEILING

SHEET CABLE LEGEND

ABBREV	MAKE	MODEL	DESCRIPTION	QTY
MC1	WEST PENN	25454BK	MIC/LINE CABLE	7

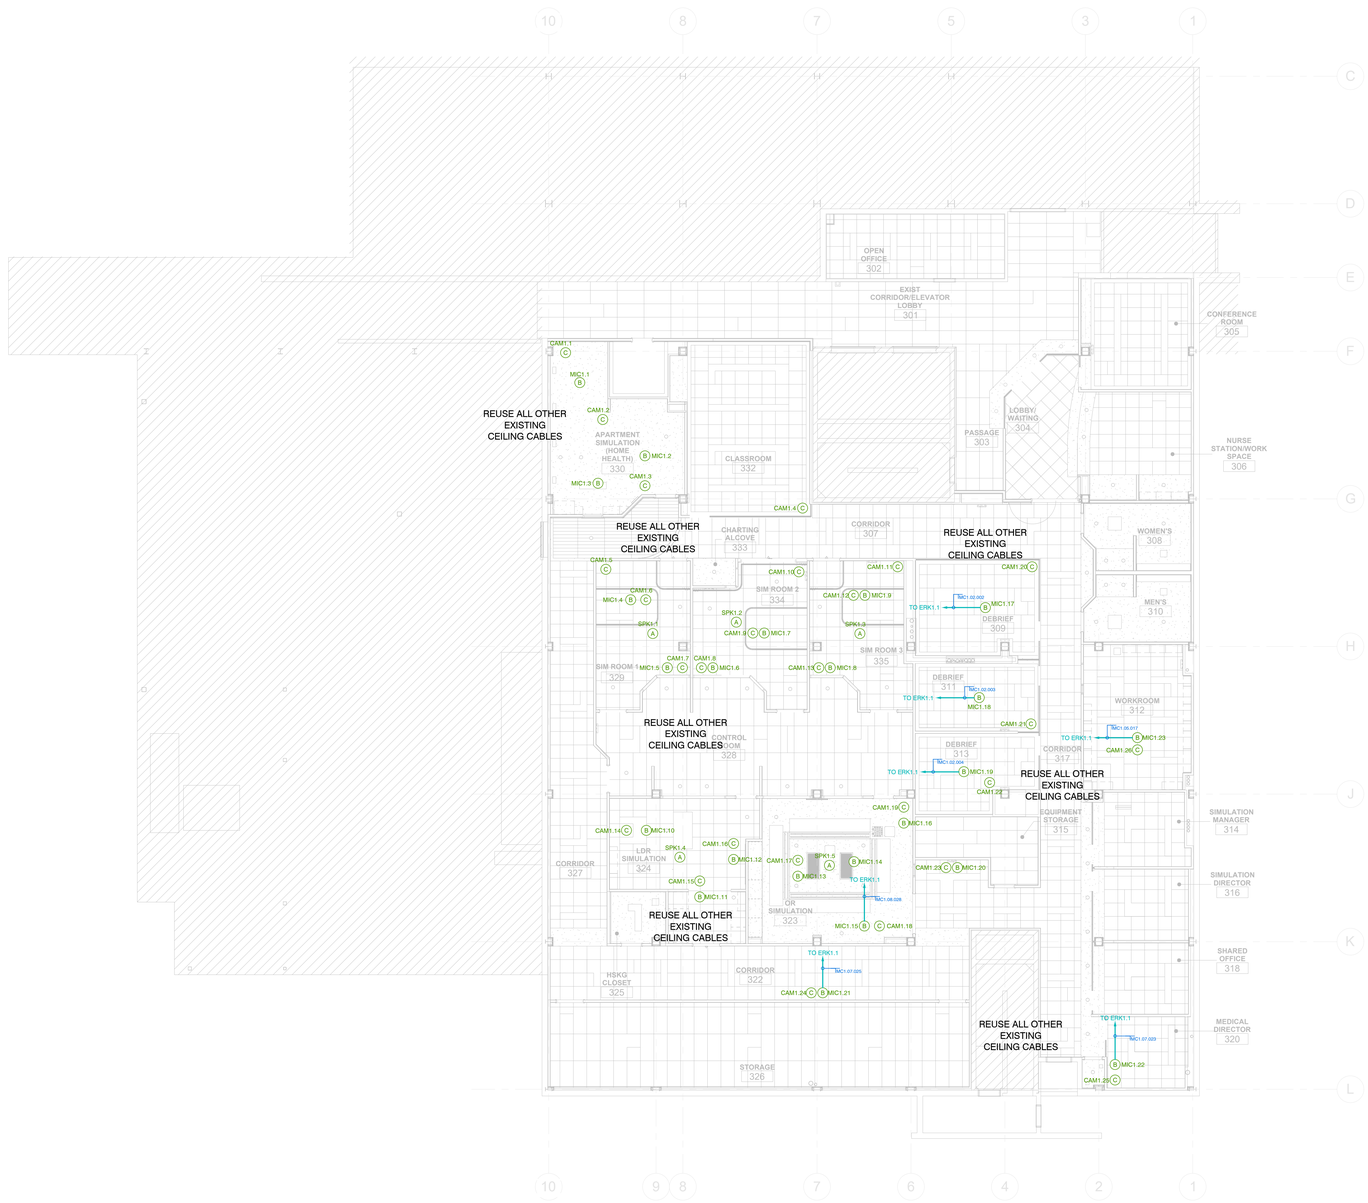

1 **SIM LAB - REFLECTED CEILING PLAN**
AUDIOVISUAL SYSTEM
SCALE: 1/8" = 1'-0"

MARSHALL INDUSTRIES

www.marshallind.com

PROJECT INFORMATION

6009

LDS HOSPITAL

SIMLAB UPDATE

CUSTOMER NAME: INTERMOUNTAIN HEALTH	CUSTOMER NUMBER: 10340
SITE NAME: LDS HOSPITAL	SITE NUMBER: 122257
SITE ADDRESS: 8TH AVENUE C STREET, SALT LAKE CITY, UT 84143	
SALES PERSON: MATT PRINTY	ENGINEERED BY: MICHAEL PLATTNER
DRAFTER: AARON SMITH	PROJECT MANAGER: DUSTIN DAVIS

DRAWING SET INFORMATION

PHASE: CONSTRUCTION

PUBLISH DATE: 3/17/2026

PLOT SIZE: ARCH FULL BLEED E (36.00 X 48.00 INCHES)

PLOT SCALE: 1' = 1'-0"

APPROVED BY: -----

SHEET REVISION INFORMATION

REVISION: ----

REVISION DATE: -----

REVISION DESCRIPTION: -----

REVISION & ISSUE HISTORY

ISSUED FOR:	REV.	DATE:
---	---	---
---	---	---
LDS HOSPITAL

WIREPATHS AND BACKBOXES

AUDIOVISUAL SYSTEM

SIM LAB - REFLECTED CEILING PLAN

AV201

FILE NAME: AV100.DWG

DEVICE	DESCRIPTION	LOCATION
AVP-0102	TPL-0101 RJ45 PLATE	TPL1.1
AVP-0103	VDS-0111 RJ45 PLATE	VDS1.1
AVP-0503	VDS-0111 RJ45 PLATE	VDS1.10
AVP-0602	VDS-0111 RJ45 PLATE	VDS1.2
AVP-0612	VDS-0111 RJ45 PLATE	VDS1.3
AVP-0622	VDS-0111 RJ45 PLATE	VDS1.4
AVP-0632	VDS-0111 RJ45 PLATE	VDS1.5
AVP-0642	VDS-0111 RJ45 PLATE	VDS1.6
AVP-0203	VDS-0111 RJ45 PLATE	VDS1.7
AVP-0213	VDS-0111 RJ45 PLATE	VDS1.8
AVP-0223	VDS-0111 RJ45 PLATE	VDS1.9

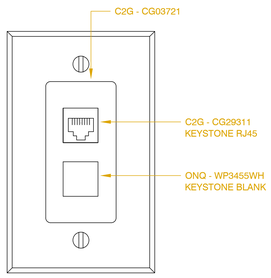

1 **C2G - CG03721**
SCALE: 1' = 1'-0"

DEVICE	DESCRIPTION	LOCATION
AVP-0601	CPU-0601 RJ45 PLATE	AVP2.1
AVP-0611	CPU-0611 RJ45 PLATE	AVP2.2
AVP-0621	CPU-0621 RJ45 PLATE	AVP2.3
AVP-0631	CPU-0631 RJ45 PLATE	AVP2.4
AVP-0641	CPU-0641 RJ45 PLATE	AVP2.5

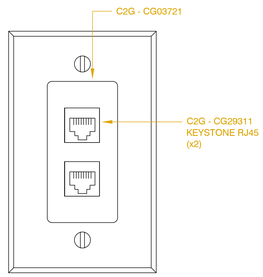

2 **AVP2**
C2G - CG03721
SCALE: 1' = 1'-0"

DEVICE	DESCRIPTION	LOCATION
AVP-0201	DEBRIEF 309 CABINET RJ45 PLATE	AVP1.2
AVP-0202	TPL-0101 RJ45 PLATE	
AVP-0211	DEBRIEF 311 CABINET RJ45 PLATE	AVP1.3
AVP-0212	TPL-0101 RJ45 PLATE	
AVP-0221	DEBRIEF 313 CABINET RJ45 PLATE	AVP1.4
AVP-0222	TPL-0101 RJ45 PLATE	

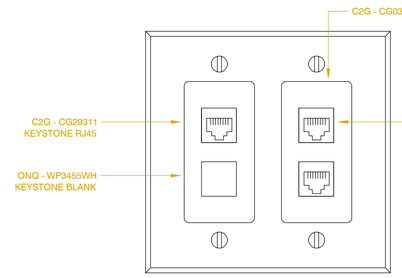

3 **AVP1**
RCI - MIKS1PW AND MIKS2PW
SCALE: 1' = 1'-0"

DEVICE	DESCRIPTION	LOCATION
AVP-0101	CLASSROOM 332 CABINET RJ45 PLATE	AVP5.1
MIP-0101	CLASSROOM 332 MIC PLATE	

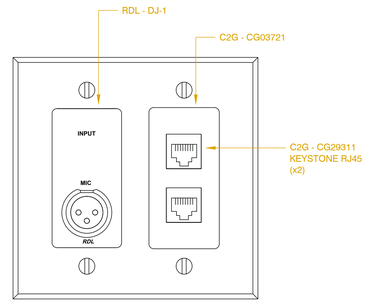

4 **AVP5**
RDL - DJ-1 AND C2G - CG03721
SCALE: 1' = 1'-0"

DEVICE	DESCRIPTION	LOCATION
AVP-0633	CTRL STATION 4 CUSTOM AV PLATE	AVP4.1

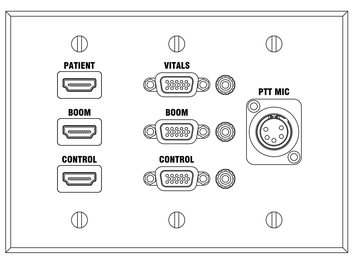

5 **AVP4**
EXISTING CONTROL ROOM WALL PLATE
SCALE: 1' = 1'-0"

DEVICE	DESCRIPTION	LOCATION
AVP-0603	CTRL STATION 1 VGA PLATE	AVP3.1
AVP-0604	CTRL STATION 1 HDMI PLATE	
MIP-0601	CTRL STATION 1 MIC INPUT PLATE	
AVP-0613	CTRL STATION 2 VGA PLATE	AVP3.2
AVP-0614	CTRL STATION 2 HDMI PLATE	
MIP-0611	CTRL STATION 2 MIC INPUT PLATE	
AVP-0623	CTRL STATION 3 VGA PLATE	AVP3.3
AVP-0624	CTRL STATION 3 HDMI PLATE	
MIP-0621	CTRL STATION 3 MIC INPUT PLATE	
AVP-0643	CTRL STATION 5 VGA PLATE	AVP3.4
AVP-0644	CTRL STATION 5 HDMI PLATE	
MIP-0641	CTRL STATION 5 MIC INPUT PLATE	

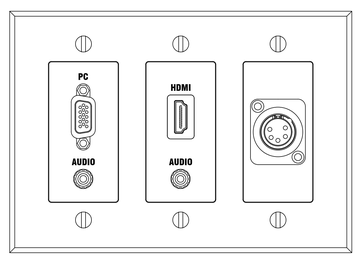

6 **AVP3**
EXISTING CONTROL STATION PLATE
SCALE: 1' = 1'-0"

MARSHALL
INDUSTRIES

www.marshallind.com

PROJECT INFORMATION

6009

LDS HOSPITAL

SIMLAB UPDATE

CUSTOMER NAME: INTERMOUNTAIN HEALTH	CUSTOMER NUMBER: 10340
SITE NAME: LDS HOSPITAL	SITE NUMBER: 122257
SITE ADDRESS: 8TH AVENUE C STREET SALT LAKE CITY, UT 84143	
SALES PERSON: MATT PRINTY	ENGINEERED BY: MICHAEL PLATTNER
DRAFTER: AARON SMITH	PROJECT MANAGER: DUSTIN DAVIS

DRAWING SET INFORMATION

PHASE: CONSTRUCTION

PUBLISH DATE: 3/17/2026

PLOT SIZE: ARCH FULL BLEED E (36.00 X 48.00 INCHES)

PLOT SCALE: 1' = 1'-0"

APPROVED BY: ----

SHEET REVISION INFORMATION

REVISION: ----

REVISION DATE: ----

REVISION DESCRIPTION: ----

REVISION & ISSUE HISTORY

ISSUED FOR:	REV.	DATE:
---	---	---
---	---	---
LDS HOSPITAL

PLATE DETAILS

SIM LAB

AUDIOVISUAL PLATES

AV701

FILE NAME: AV700.DWG

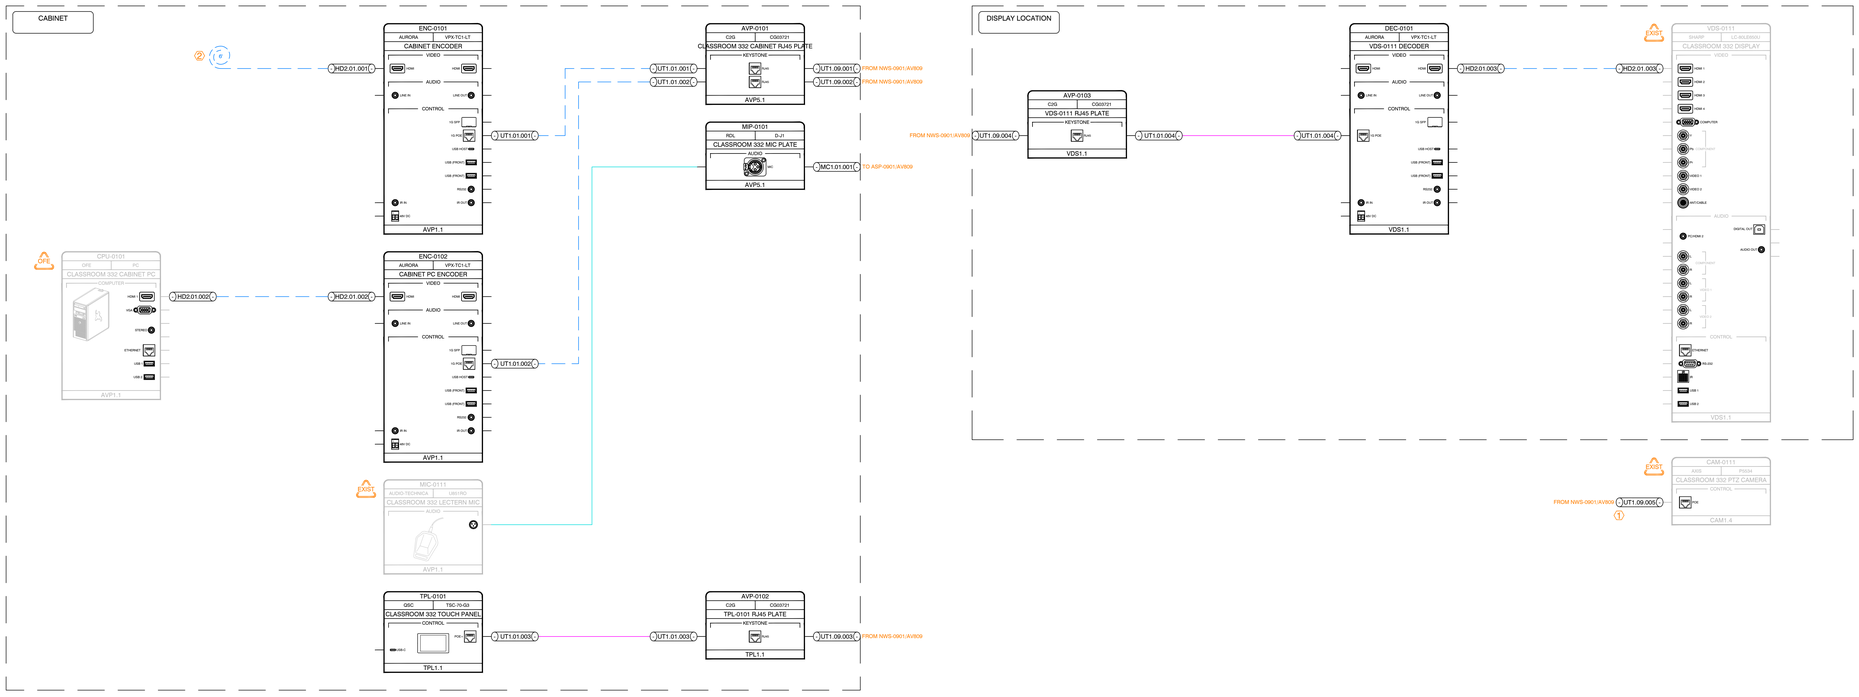

NUM	NOTES
1	REUSE EXISTING CABLE.
2	COIL ON TABLE.
3	-
4	-
5	-
6	-
7	-

LINE DESIGNATIONS KEY

- BULK - AUDIO
- PATCH - AUDIO
- BULK - VIDEO
- PATCH - VIDEO
- BULK - CONTROL
- PATCH - CONTROL
- BULK - EXISTING
- PATCH - EXISTING

MARSHALL INDUSTRIES

www.marshallind.com

PROJECT INFORMATION

6009

LDS HOSPITAL

SIMLAB UPDATE

CUSTOMER NAME: INTERMOUNTAIN HEALTH	CUSTOMER NUMBER: 10340
SITE NAME: LDS HOSPITAL	SITE NUMBER: 122257
SITE ADDRESS: 8TH AVENUE C STREET SALT LAKE CITY, UT 84143	
SALES PERSON: MATT PRINTY	ENGINEERED BY: MICHAEL PLATTNER
DRAFTER: AARON SMITH	PROJECT MANAGER: DUSTIN DAVIS

DRAWING SET INFORMATION

PHASE: CONSTRUCTION

PUBLISH DATE: 3/17/2026

PLOT SIZE: ARCH FULL BLEED E (36.00 X 48.00 INCHES)

PLOT SCALE: 1' = 1'-0"

APPROVED BY: -----

SHEET REVISION INFORMATION

REVISION:	REVISION DATE:	REVISION DESCRIPTION:
----	-----	-----

REVISION & ISSUE HISTORY

ISSUED FOR:	REV.	DATE:
---	---	---
---	---	---
LDS HOSPITAL

SINGLE LINE DIAGRAMS

CLASSROOM 332

AV SYSTEM FUNCTIONAL

AV801

FILE NAME: AV800.DWG

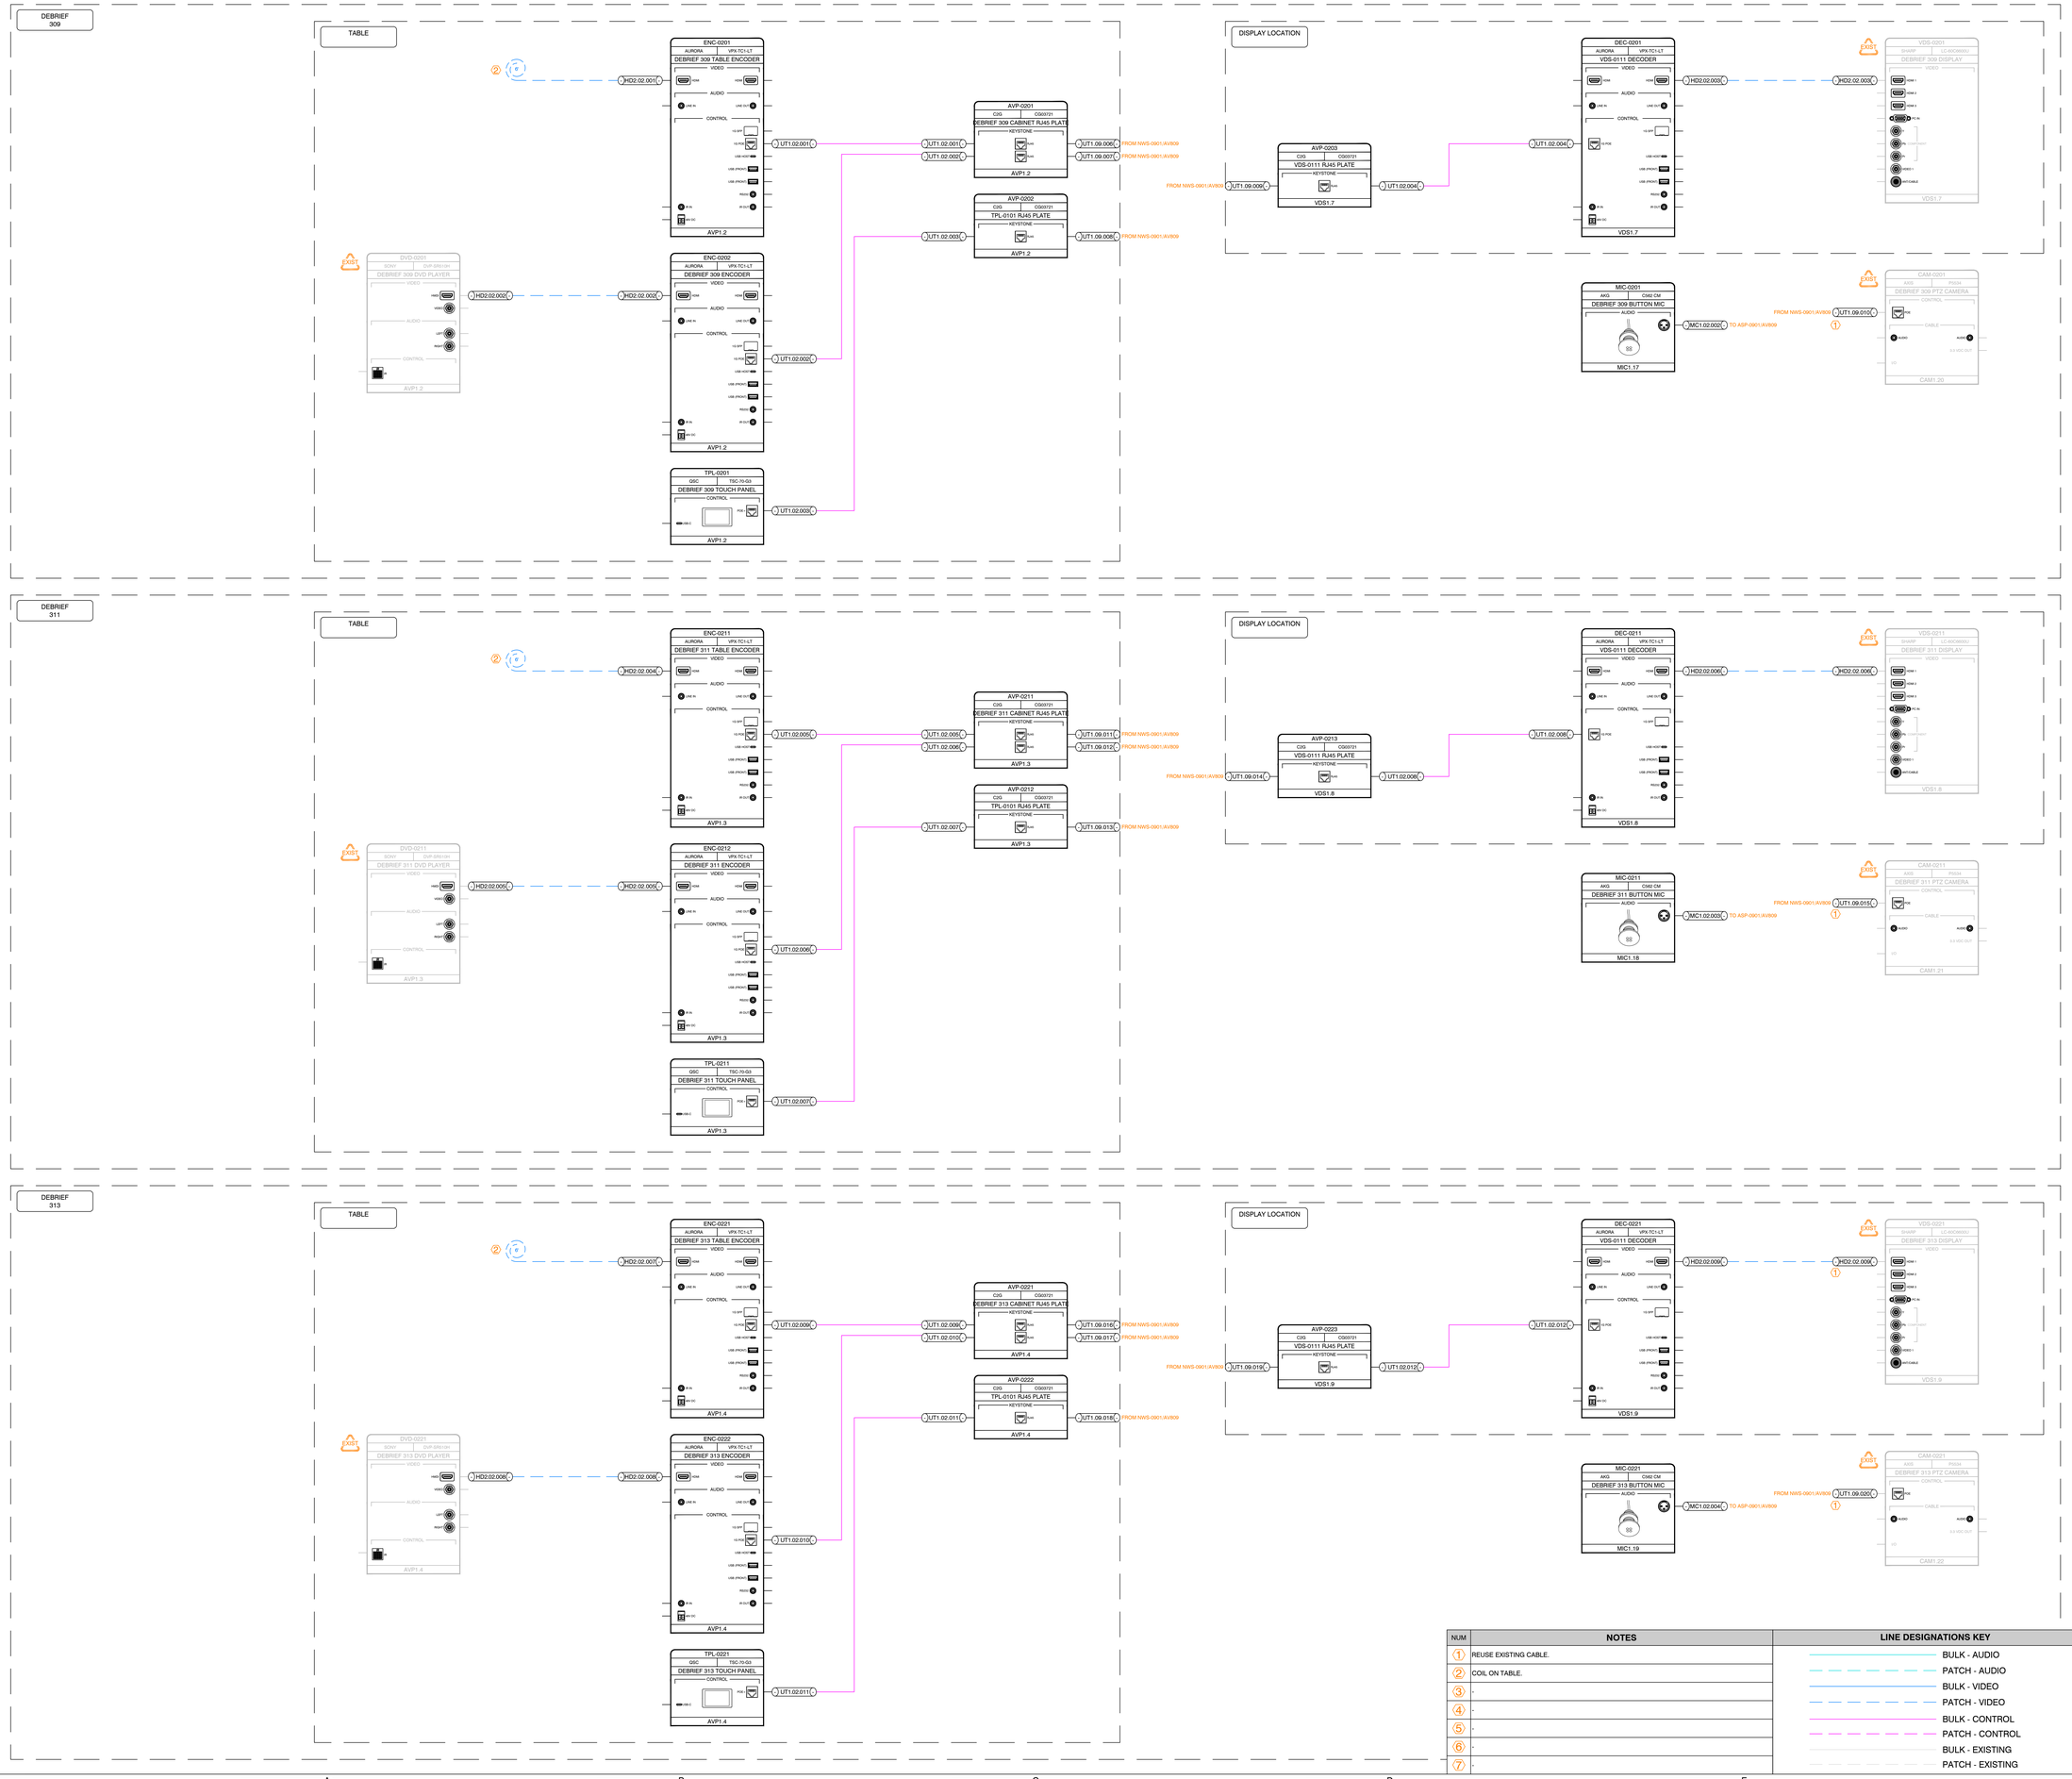

NUM	NOTES
1	REUSE EXISTING CABLE.
2	COIL ON TABLE.
3	-
4	-
5	-
6	-
7	-

LINE DESIGNATIONS KEY
BULK - AUDIO
PATCH - AUDIO
BULK - VIDEO
PATCH - VIDEO
BULK - CONTROL
PATCH - CONTROL
BULK - EXISTING
PATCH - EXISTING

MARSHALL INDUSTRIES

www.marshallind.com

PROJECT INFORMATION

6009

LDS HOSPITAL

SIMLAB UPDATE

CUSTOMER NAME: INTERMOUNTAIN HEALTH	CUSTOMER NUMBER: 10340
SITE NAME: LDS HOSPITAL	SITE NUMBER: 122257
SITE ADDRESS: 8TH AVENUE C STREET SALT LAKE CITY, UT 84143	
SALES PERSON: MATT PRINTY	ENGINEERED BY: MICHAEL PLATTNER
DRAFTER: AARON SMITH	PROJECT MANAGER: DUSTIN DAVIS

DRAWING SET INFORMATION

PHASE: CONSTRUCTION

PUBLISH DATE: 3/17/2026

PLOT SIZE: ARCH FULL BLEED E (36.00 X 48.00 INCHES)

PLOT SCALE: 1' = 1'-0"

APPROVED BY: -----

SHEET REVISION INFORMATION

REVISION:	REVISION DATE:	-----
---	REVISION DESCRIPTION:	-----

REVISION & ISSUE HISTORY

ISSUED FOR:	REV.	DATE:
---	---	---
---	---	---
LDS HOSPITAL

SINGLE LINE DIAGRAMS

DEBRIEF ROOMS

AV SYSTEM FUNCTIONAL

AV802

FILE NAME: AV800.DWG

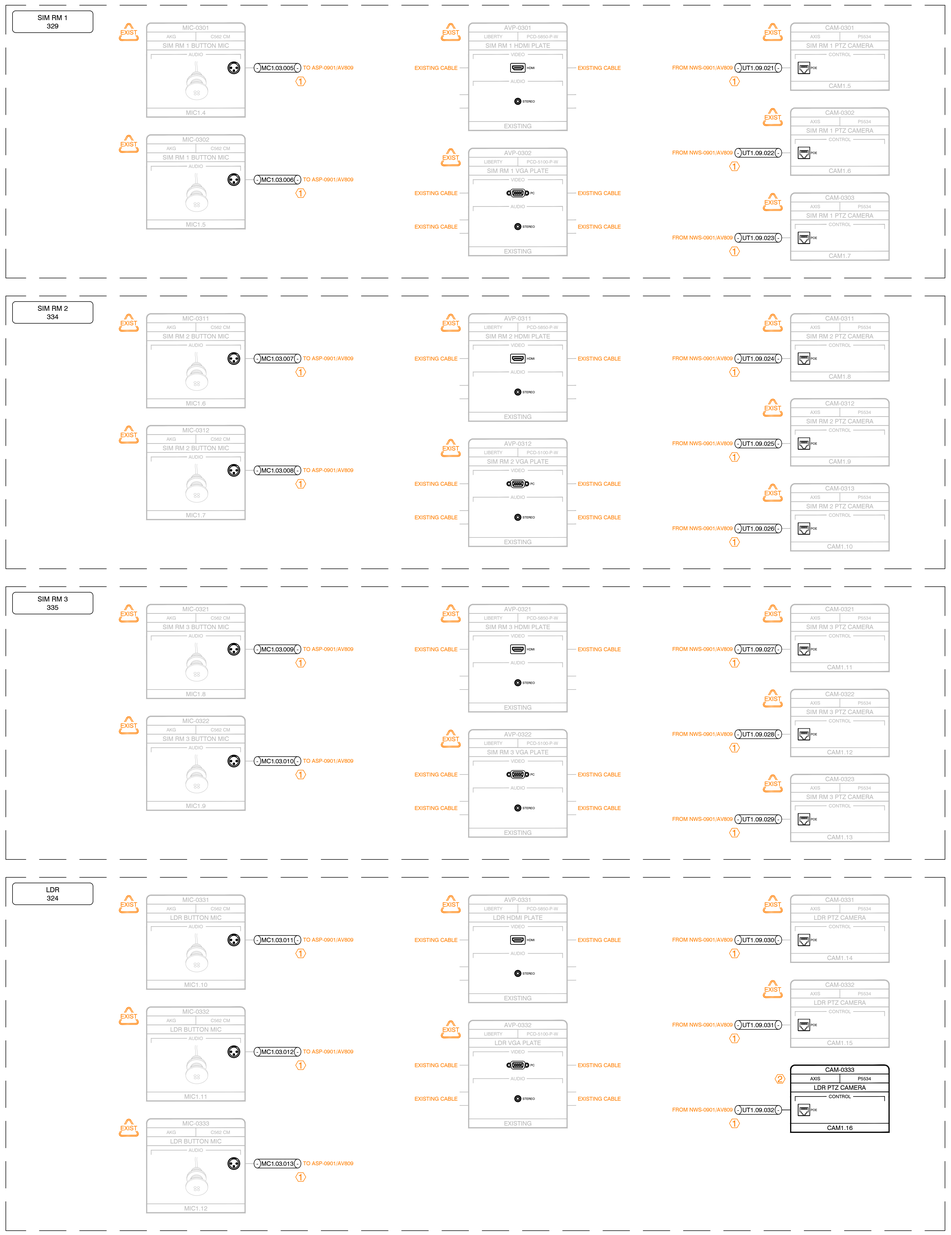

NUM	NOTES
1	REUSE EXISTING CABLE.
2	PLACE WHICHEVER LDR CAMERA IS GOING BAD.
3	-
4	-
5	-
6	-
7	-

LINE DESIGNATIONS KEY
BULK - AUDIO
PATCH - AUDIO
BULK - VIDEO
PATCH - VIDEO
BULK - CONTROL
PATCH - CONTROL
BULK - EXISTING
PATCH - EXISTING

MARSHALL INDUSTRIES

www.marshallind.com

PROJECT INFORMATION

6009

LDS HOSPITAL

SIMLAB UPDATE

CUSTOMER NAME: INTERMOUNTAIN HEALTH	CUSTOMER NUMBER: 10340
SITE NAME: LDS HOSPITAL	SITE NUMBER: 122257
SITE ADDRESS: 8TH AVENUE C STREET, SALT LAKE CITY, UT 84143	
SALES PERSON: MATT PRINTY	ENGINEERED BY: MICHAEL PLATTNER
DRAFTER: AARON SMITH	PROJECT MANAGER: DUSTIN DAVIS

DRAWING SET INFORMATION

PHASE: CONSTRUCTION

PUBLISH DATE: 3/17/2026

PLOT SIZE: ARCH FULL BLEED E (36.00 X 48.00 INCHES)

PLOT SCALE: 1' = 1'-0"

APPROVED BY: ----

SHEET REVISION INFORMATION

REVISION: ----

REVISION DATE: ----

REVISION DESCRIPTION: ----

REVISION & ISSUE HISTORY

ISSUED FOR:	REV.	DATE:
---	---	---
---	---	---
LDS HOSPITAL

SINGLE LINE DIAGRAMS

SIM LABS

AV SYSTEM FUNCTIONAL

AV803

FILE NAME: AV800.DWG

NUM	NOTES
1	REUSE EXISTING CABLE.
2	-
3	-
4	-
5	-
6	-
7	-

LINE DESIGNATIONS KEY
BULK - AUDIO
PATCH - AUDIO
BULK - VIDEO
PATCH - VIDEO
BULK - CONTROL
PATCH - CONTROL
BULK - EXISTING
PATCH - EXISTING

MARSHALL INDUSTRIES

www.marshallind.com

PROJECT INFORMATION

6009

LDS HOSPITAL

SIMLAB UPDATE

CUSTOMER NAME: INTERMOUNTAIN HEALTH	CUSTOMER NUMBER: 10340
SITE NAME: LDS HOSPITAL	SITE NUMBER: 122257
SITE ADDRESS: 8TH AVENUE C STREET, SALT LAKE CITY, UT 84143	
SALES PERSON: MATT PRINTY	ENGINEERED BY: MICHAEL PLATTNER
DRAFTER: AARON SMITH	PROJECT MANAGER: DUSTIN DAVIS

DRAWING SET INFORMATION

PHASE: CONSTRUCTION

PUBLISH DATE: 3/17/2026

PLOT SIZE: ARCH FULL BLEED E (36.00 X 48.00 INCHES)

PLOT SCALE: 1' = 1'-0"

APPROVED BY: -----

SHEET REVISION INFORMATION

REVISION: ----

REVISION DATE: -----

REVISION DESCRIPTION: -----

REVISION & ISSUE HISTORY

ISSUED FOR:	REV.	DATE:
---	---	---
---	---	---
LDS HOSPITAL

SINGLE LINE DIAGRAMS

APARTMENT 330

AV SYSTEM FUNCTIONAL

AV804

FILE NAME: AV800.DWG

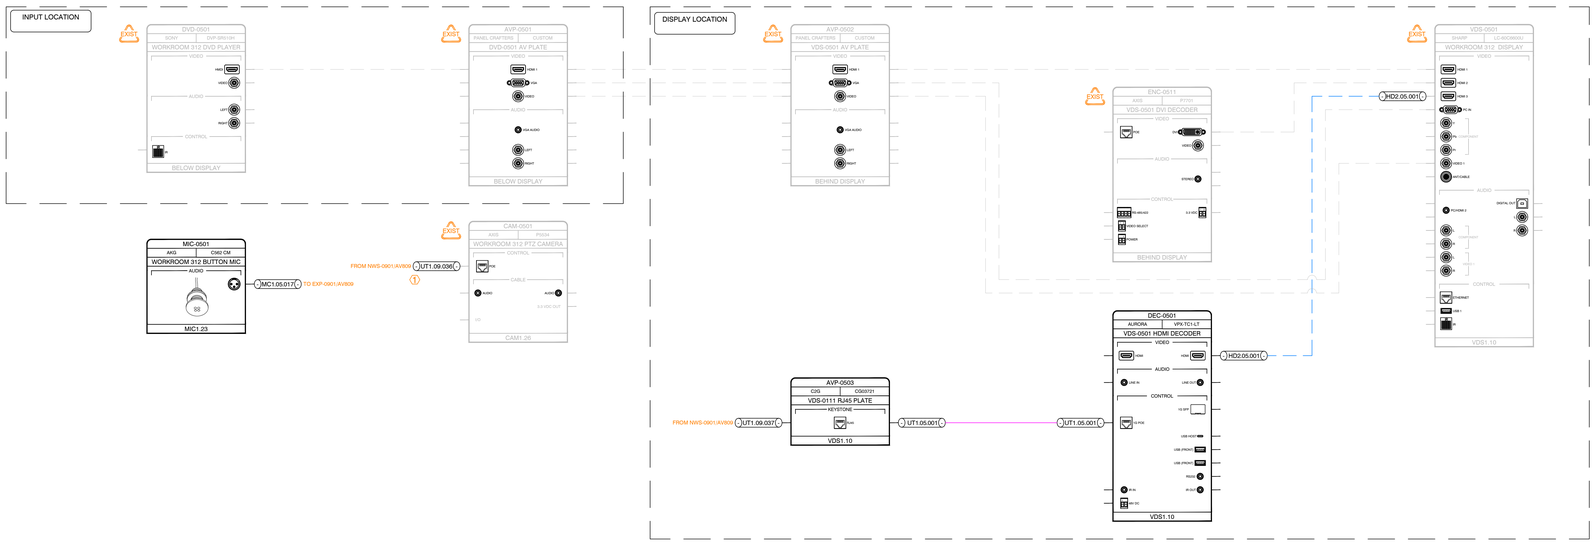

NUM	NOTES
1	REUSE EXISTING CABLE.
2	-
3	-
4	-
5	-
6	-
7	-

LINE DESIGNATIONS KEY
BULK - AUDIO
PATCH - AUDIO
BULK - VIDEO
PATCH - VIDEO
BULK - CONTROL
PATCH - CONTROL
BULK - EXISTING
PATCH - EXISTING

MARSHALL INDUSTRIES

www.marshallind.com

PROJECT INFORMATION

6009

LDS HOSPITAL

SIMLAB UPDATE

CUSTOMER NAME: INTERMOUNTAIN HEALTH	CUSTOMER NUMBER: 10340
SITE NAME: LDS HOSPITAL	SITE NUMBER: 122257
SITE ADDRESS: 8TH AVENUE C STREET SALT LAKE CITY, UT 84143	
SALES PERSON: MATT PRINTY	ENGINEERED BY: MICHAEL PLATTNER
DRAFTER: AARON SMITH	PROJECT MANAGER: DUSTIN DAVIS

DRAWING SET INFORMATION

PHASE: CONSTRUCTION

PUBLISH DATE: 3/17/2026

PLOT SIZE: ARCH FULL BLEED E (36.00 X 48.00 INCHES)

PLOT SCALE: 1' = 1'-0"

APPROVED BY: -----

SHEET REVISION INFORMATION

REVISION:	REVISION DATE:
----	REVISION DESCRIPTION: -----

REVISION & ISSUE HISTORY

ISSUED FOR:	REV.	DATE:
---	---	---
---	---	---
LDS HOSPITAL

SINGLE LINE DIAGRAMS

WORKROOM 312

AV SYSTEM FUNCTIONAL

AV805

FILE NAME: AV800.DWG

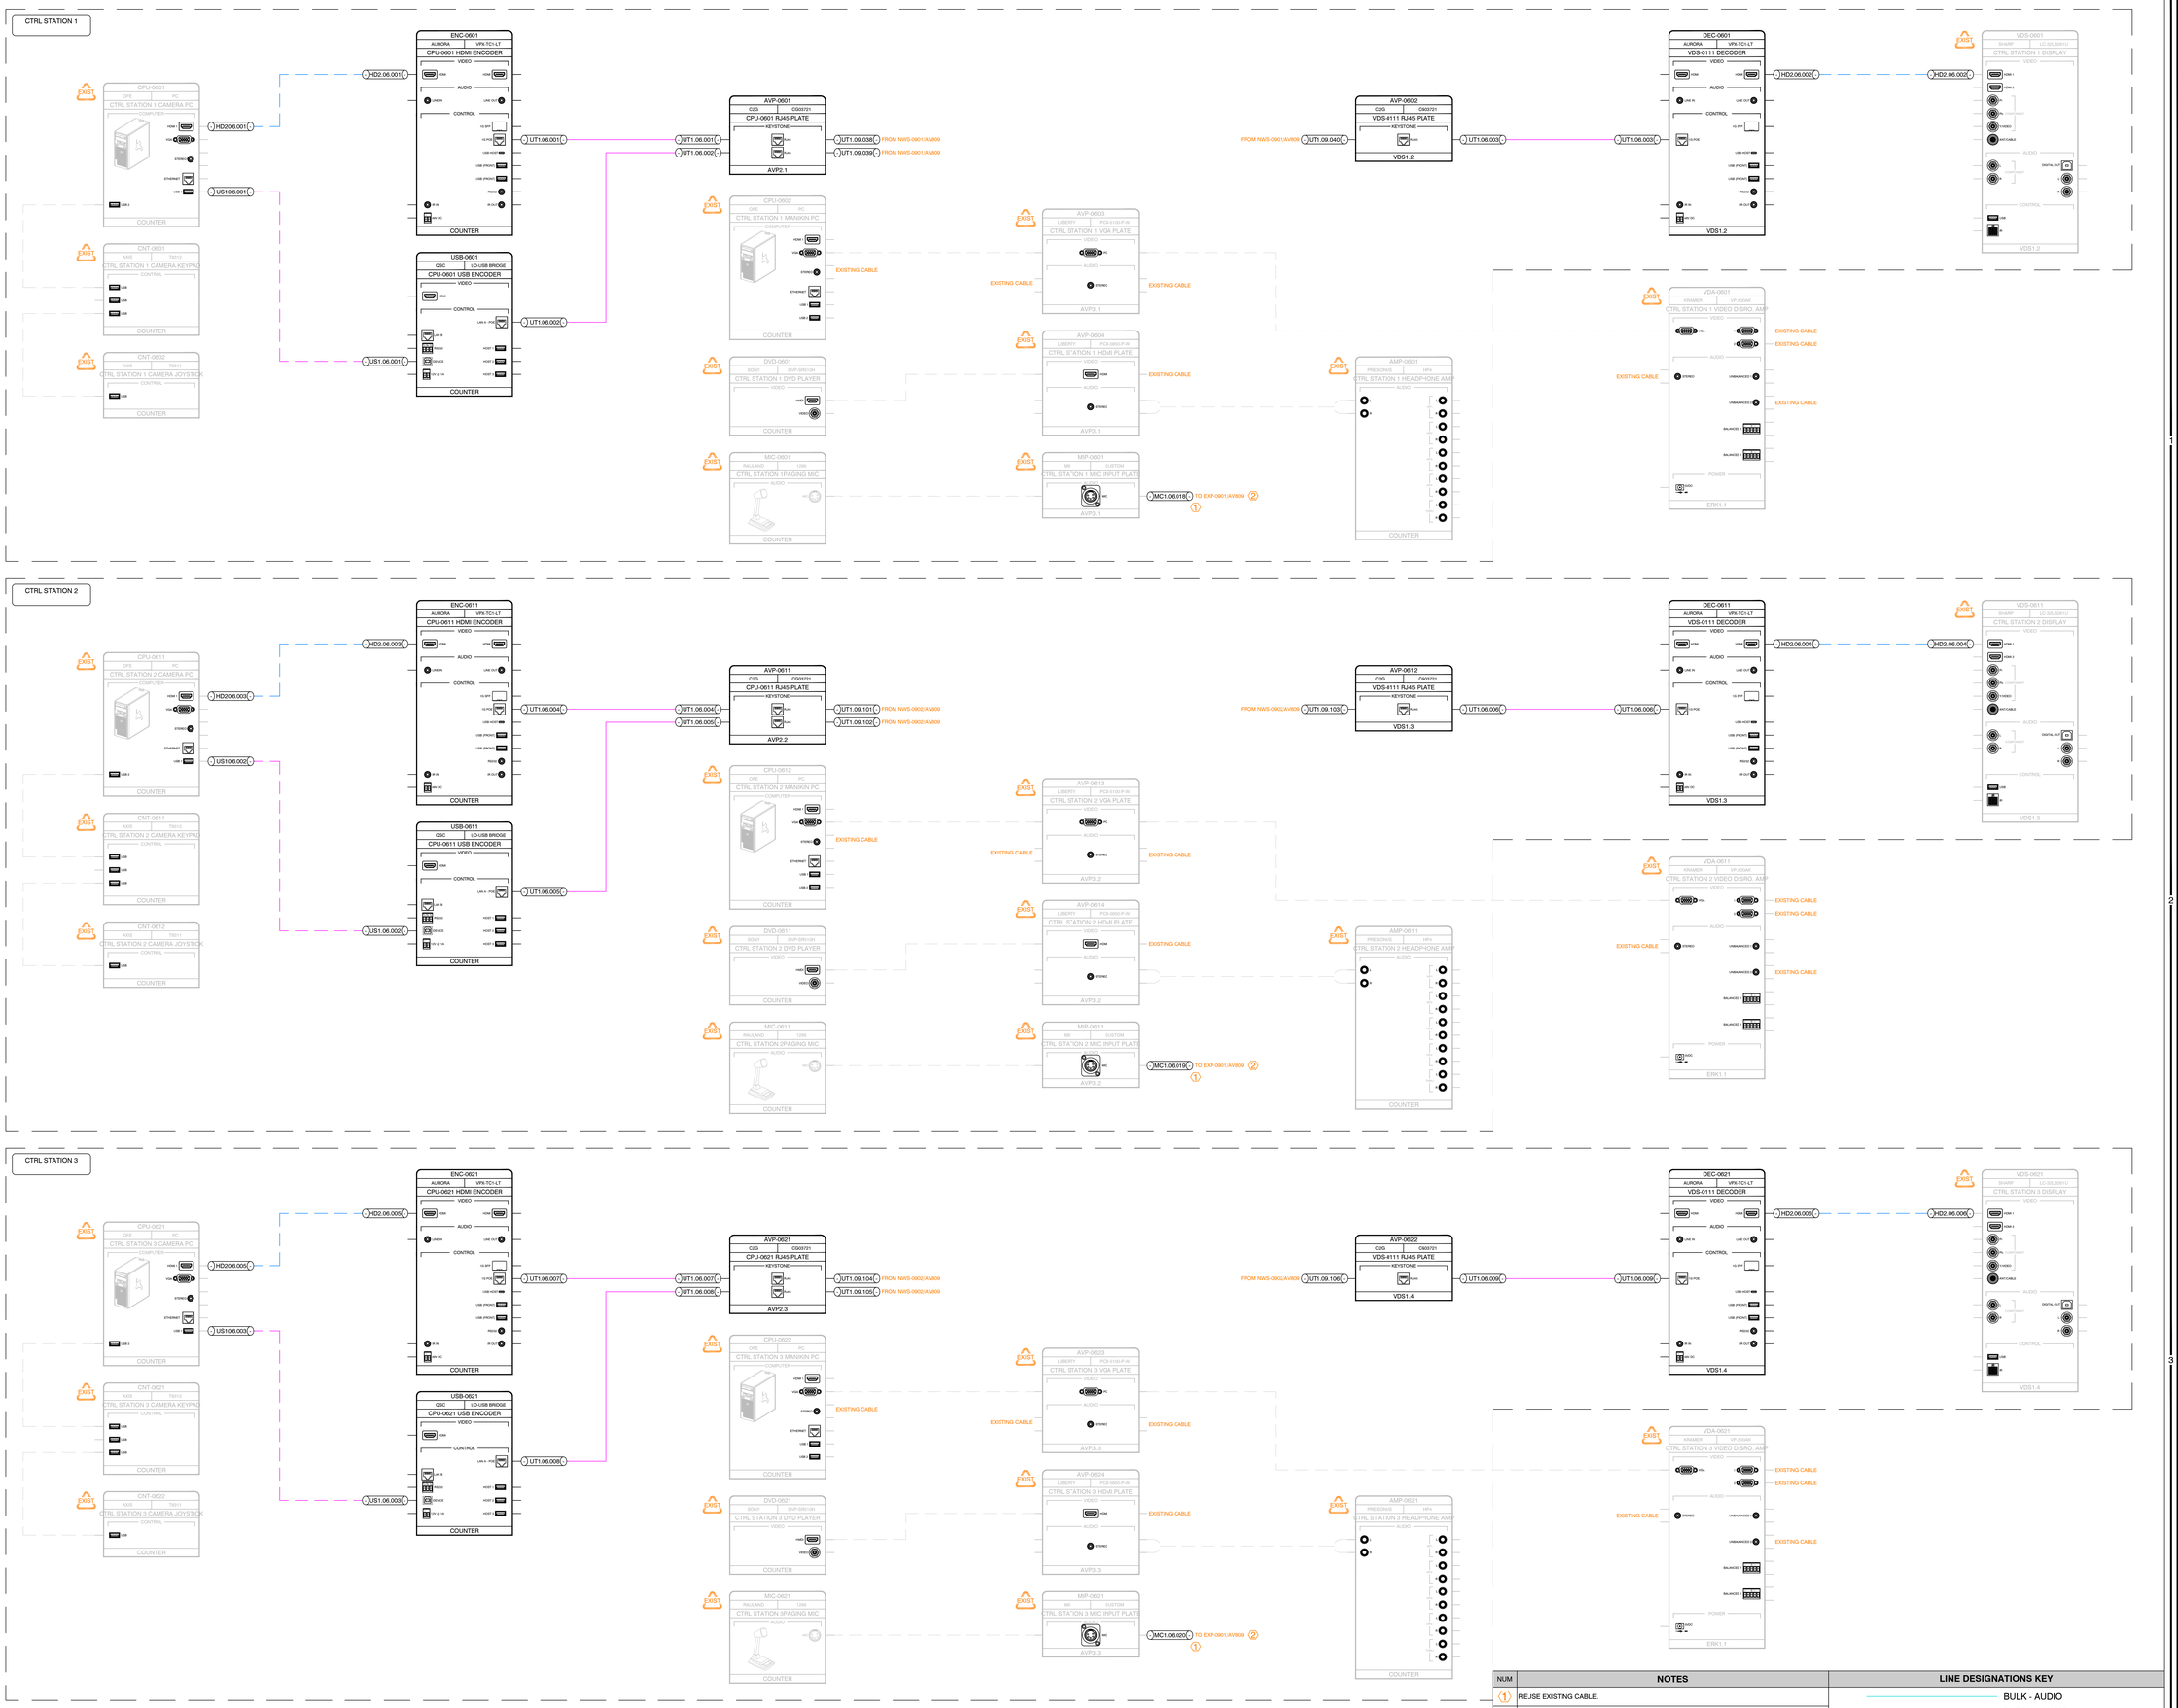

NUM	NOTES
①	REUSE EXISTING CABLE.
②	NON-AEC INPUT ON QSC DSP
③	-
④	-
⑤	-
⑥	-
⑦	-

LINE DESIGNATIONS KEY

- BULK - AUDIO
- PATCH - AUDIO
- BULK - VIDEO
- PATCH - VIDEO
- BULK - CONTROL
- PATCH - CONTROL
- BULK - EXISTING
- PATCH - EXISTING

MARSHALL INDUSTRIES

www.marshallind.com

PROJECT INFORMATION

6009

LDS HOSPITAL

SIMLAB UPDATE

CUSTOMER NAME: INTERMOUNTAIN HEALTH	CUSTOMER NUMBER: 10340
SITE NAME: LDS HOSPITAL	SITE NUMBER: 122257

SITE ADDRESS:
8TH AVENUE C STREET
SALT LAKE CITY, UT 84143

SALES PERSON: MATT PRINTY	ENGINEERED BY: MICHAEL PLATTNER
DRAFTER: AARON SMITH	PROJECT MANAGER: DUSTIN DAVIS

DRAWING SET INFORMATION

PHASE: CONSTRUCTION

PUBLISH DATE: 3/17/2026

PLOT SIZE: ARCH FULL BLEED E (36.00 X 48.00 INCHES)

PLOT SCALE: 1' = 1'-0"

APPROVED BY: -----

SHEET REVISION INFORMATION

REVISION:	REVISION DATE:	REVISION DESCRIPTION:
---	-----	-----

REVISION & ISSUE HISTORY

ISSUED FOR:	REV.	DATE:
---	---	---
---	---	---
LDS HOSPITAL

SINGLE LINE DIAGRAMS

CONTROL ROOM 328

AV SYSTEM FUNCTIONAL

AV806.1

FILE NAME: AV800.DWG

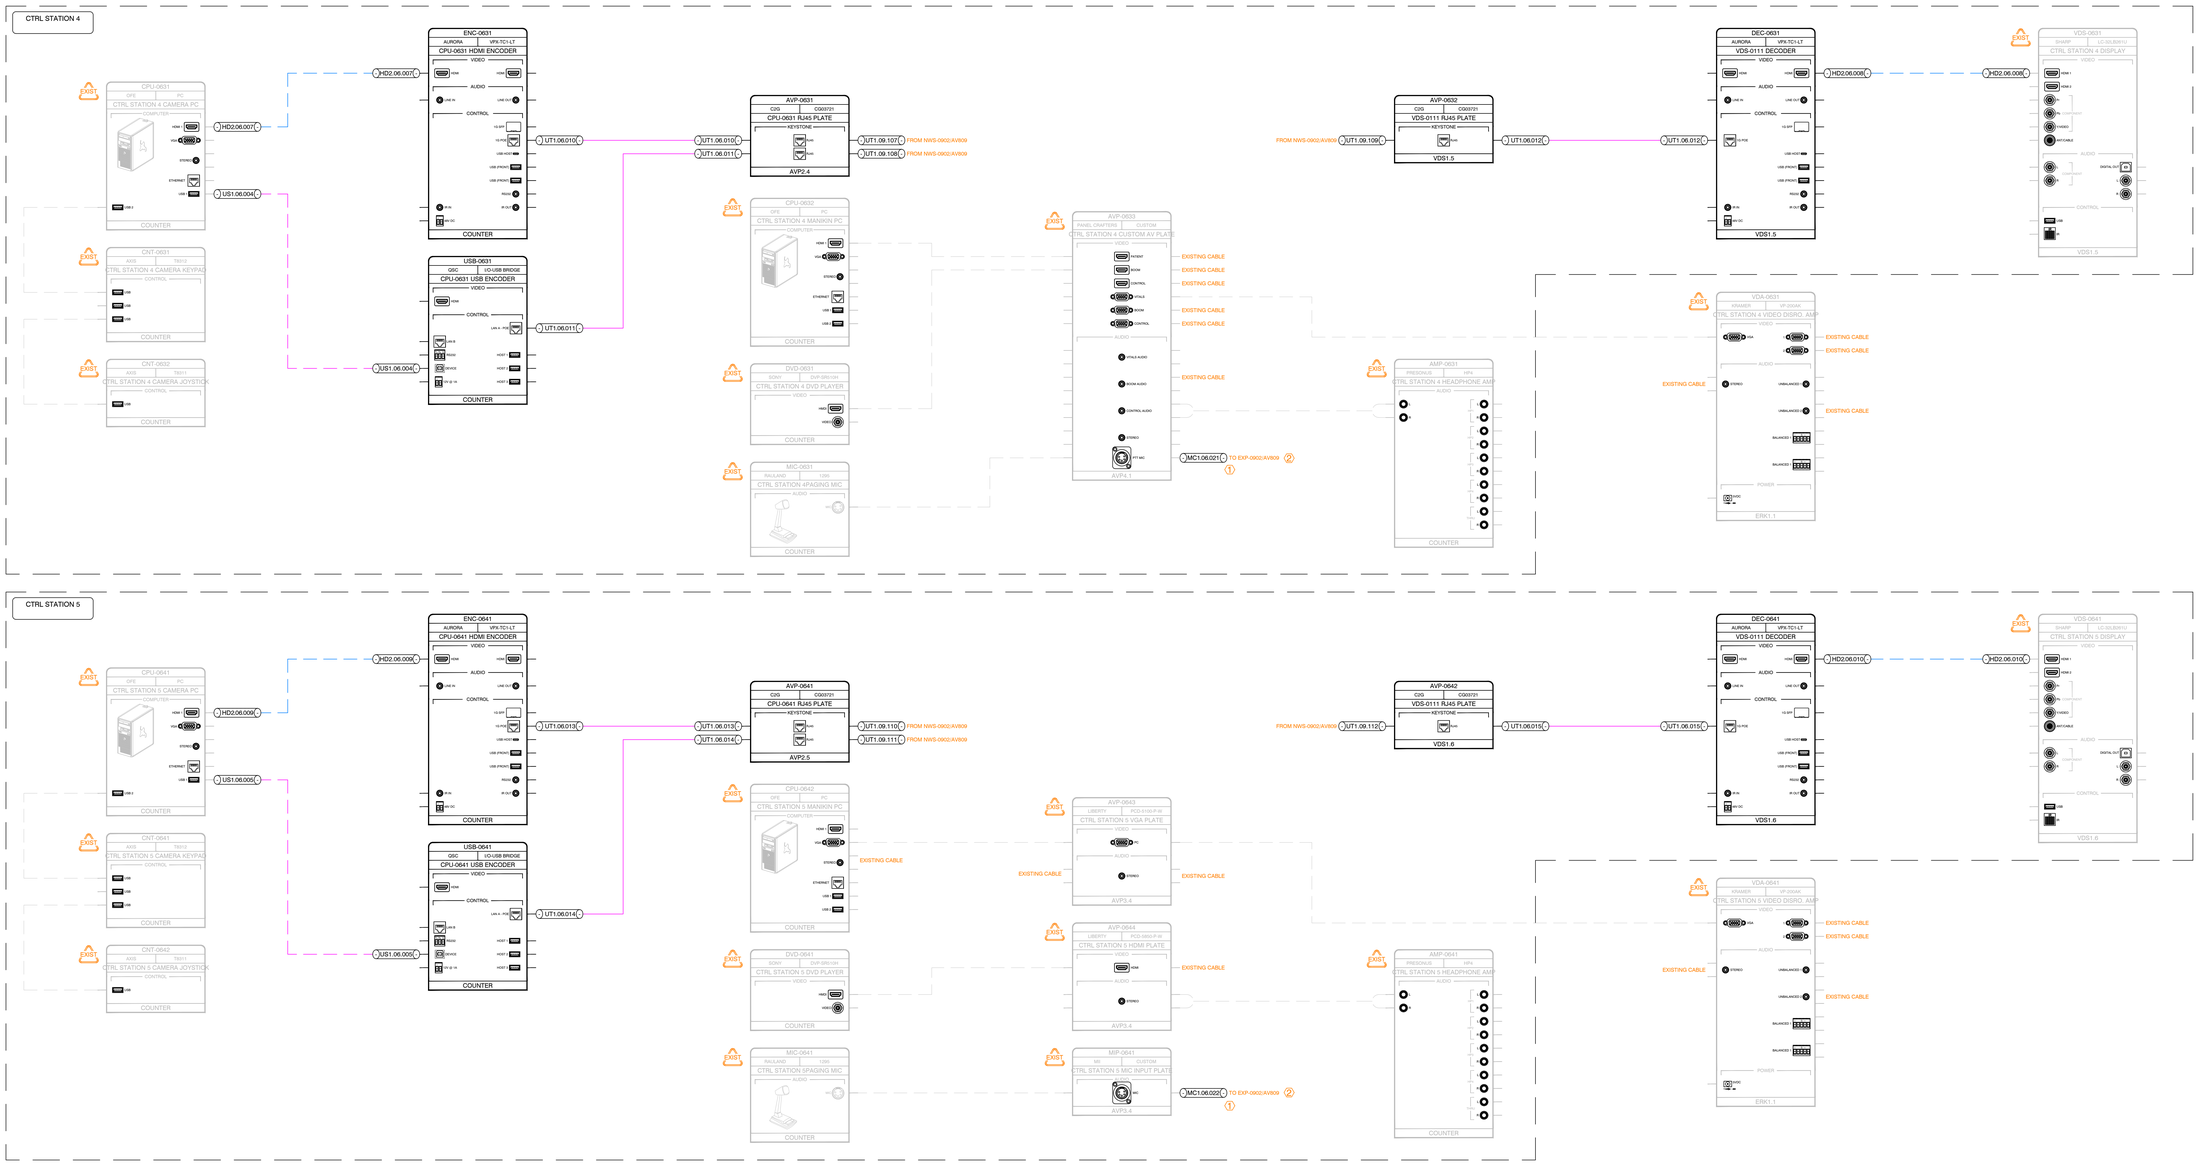

NUM	NOTES
1	REUSE EXISTING CABLE.
2	NON-AEC INPUT ON QSC DSP
3	-
4	-
5	-
6	-
7	-

LINE DESIGNATIONS KEY

- BULK - AUDIO
- PATCH - AUDIO
- BULK - VIDEO
- PATCH - VIDEO
- BULK - CONTROL
- PATCH - CONTROL
- BULK - EXISTING
- PATCH - EXISTING

MARSHALL INDUSTRIES

www.marshallind.com

PROJECT INFORMATION

6009

LDS HOSPITAL

SIMLAB UPDATE

CUSTOMER NAME: INTERMOUNTAIN HEALTH	CUSTOMER NUMBER: 10340
SITE NAME: LDS HOSPITAL	SITE NUMBER: 122257

SITE ADDRESS:
8TH AVENUE C STREET
SALT LAKE CITY, UT 84143

SALES PERSON: MATT PRINTY	ENGINEERED BY: MICHAEL PLATTNER
DRAFTER: AARON SMITH	PROJECT MANAGER: DUSTIN DAVIS

DRAWING SET INFORMATION

PHASE: CONSTRUCTION

PUBLISH DATE: 3/17/2026

PLOT SIZE: ARCH FULL BLEED E (36.00 X 48.00 INCHES)

PLOT SCALE: 1' = 1'-0"

APPROVED BY: -----

SHEET REVISION INFORMATION

REVISION:	REVISION DATE:	REVISION DESCRIPTION:
---	-----	-----

REVISION & ISSUE HISTORY

ISSUED FOR:	REV.	DATE:
---	---	---
---	---	---
LDS HOSPITAL

SINGLE LINE DIAGRAMS

CONTROL ROOM 328

AV SYSTEM FUNCTIONAL

AV806.2

FILE NAME: AV800.DWG

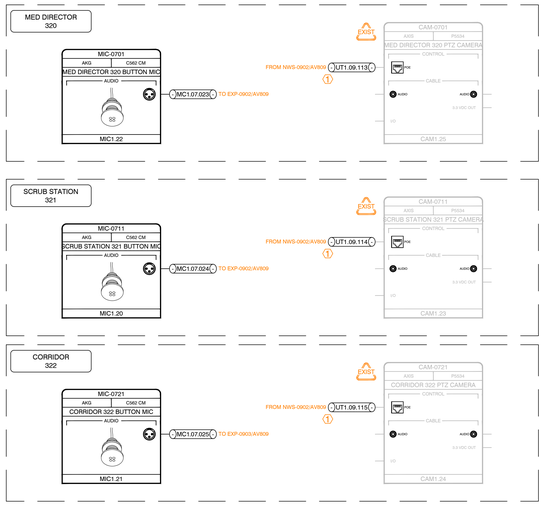

NUM	NOTES
1	REUSE EXISTING CABLE.
2	-
3	-
4	-
5	-
6	-
7	-

LINE DESIGNATIONS KEY

- BULK - AUDIO
- PATCH - AUDIO
- BULK - VIDEO
- PATCH - VIDEO
- BULK - CONTROL
- PATCH - CONTROL
- BULK - EXISTING
- PATCH - EXISTING

MARSHALL INDUSTRIES

www.marshallind.com

PROJECT INFORMATION

6009

LDS HOSPITAL

SIMLAB UPDATE

CUSTOMER NAME: INTERMOUNTAIN HEALTH	CUSTOMER NUMBER: 10340
SITE NAME: LDS HOSPITAL	SITE NUMBER: 122257
SITE ADDRESS: 8TH AVENUE C STREET, SALT LAKE CITY, UT 84143	
SALES PERSON: MATT PRINTY	ENGINEERED BY: MICHAEL PLATTNER
DRAFTER: AARON SMITH	PROJECT MANAGER: DUSTIN DAVIS

DRAWING SET INFORMATION

PHASE: CONSTRUCTION

PUBLISH DATE: 3/17/2026

PLOT SIZE: ARCH FULL BLEED E (36.00 X 48.00 INCHES)

PLOT SCALE: 1' = 1'-0"

APPROVED BY: -----

SHEET REVISION INFORMATION

REVISION: ----

REVISION DATE: -----

REVISION DESCRIPTION: -----

REVISION & ISSUE HISTORY

ISSUED FOR:	REV.	DATE:
---	---	---
---	---	---
LDS HOSPITAL

SINGLE LINE DIAGRAMS

ROOMS 320, 321, AND 322

AV SYSTEM FUNCTIONAL

AV807

FILE NAME: AV800.DWG

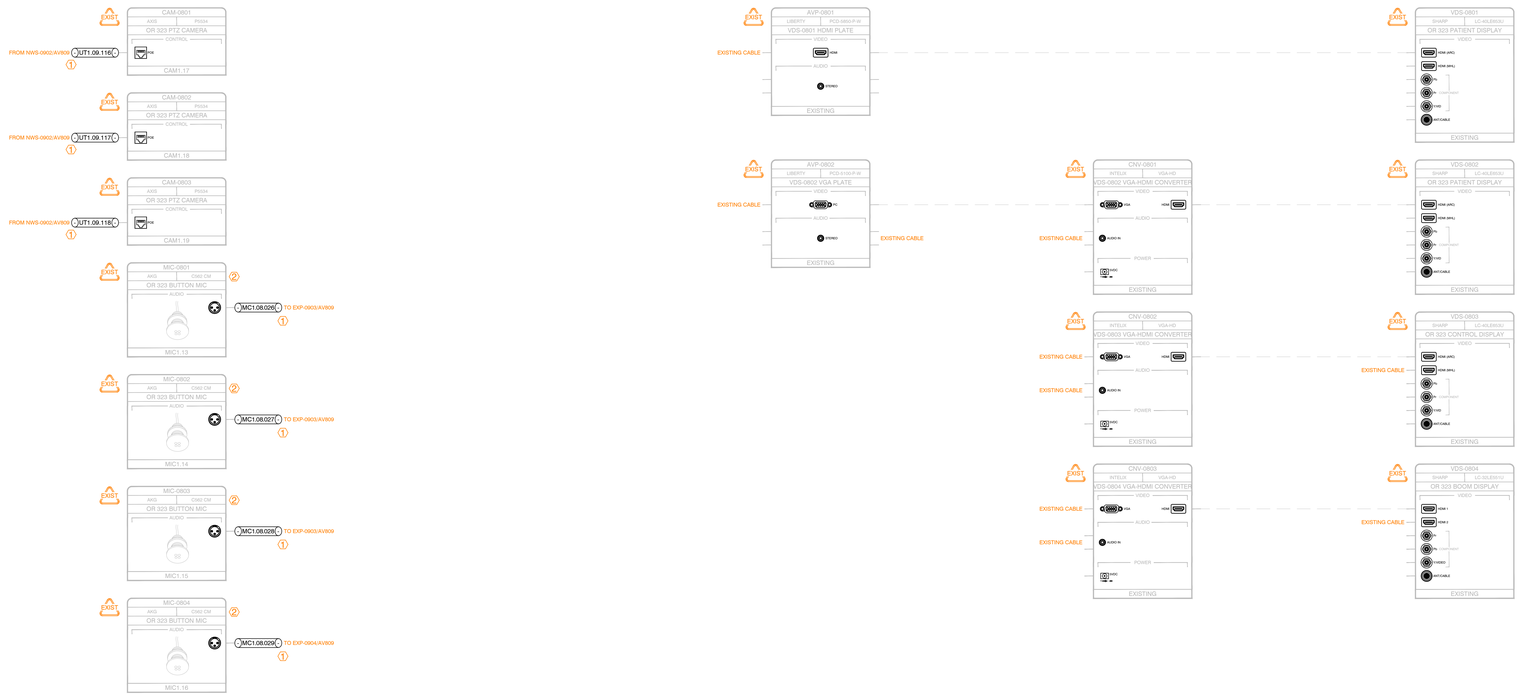

NUM	NOTES
1	REUSE EXISTING CABLE.
2	ONLY 3 BUTTON MICS USED. COORDINATE WITH OWNER WHICH ONE TO REMOVE.
3	-
4	-
5	-
6	-
7	-

LINE DESIGNATIONS KEY
BULK - AUDIO
PATCH - AUDIO
BULK - VIDEO
PATCH - VIDEO
BULK - CONTROL
PATCH - CONTROL
BULK - EXISTING
PATCH - EXISTING

MARSHALL INDUSTRIES

www.marshallind.com

PROJECT INFORMATION

6009

LDS HOSPITAL

SIMLAB UPDATE

CUSTOMER NAME: INTERMOUNTAIN HEALTH	CUSTOMER NUMBER: 10340
SITE NAME: LDS HOSPITAL	SITE NUMBER: 122257
SITE ADDRESS: 8TH AVENUE C STREET SALT LAKE CITY, UT 84143	
SALES PERSON: MATT PRINTY	ENGINEERED BY: MICHAEL PLATTNER
DRAFTER: AARON SMITH	PROJECT MANAGER: DUSTIN DAVIS

DRAWING SET INFORMATION

PHASE: CONSTRUCTION

PUBLISH DATE: 3/17/2026

PLOT SIZE: ARCH FULL BLEED E (36.00 X 48.00 INCHES)

PLOT SCALE: 1' = 1'-0"

APPROVED BY: -----

SHEET REVISION INFORMATION

REVISION:	REVISION DATE:	REVISION DESCRIPTION:
----	-----	-----

REVISION & ISSUE HISTORY

ISSUED FOR:	REV.	DATE:
---	---	---
---	---	---
LDS HOSPITAL

SINGLE LINE DIAGRAMS

OR 323

AV SYSTEM FUNCTIONAL

AV808

FILE NAME: AV800.DWG

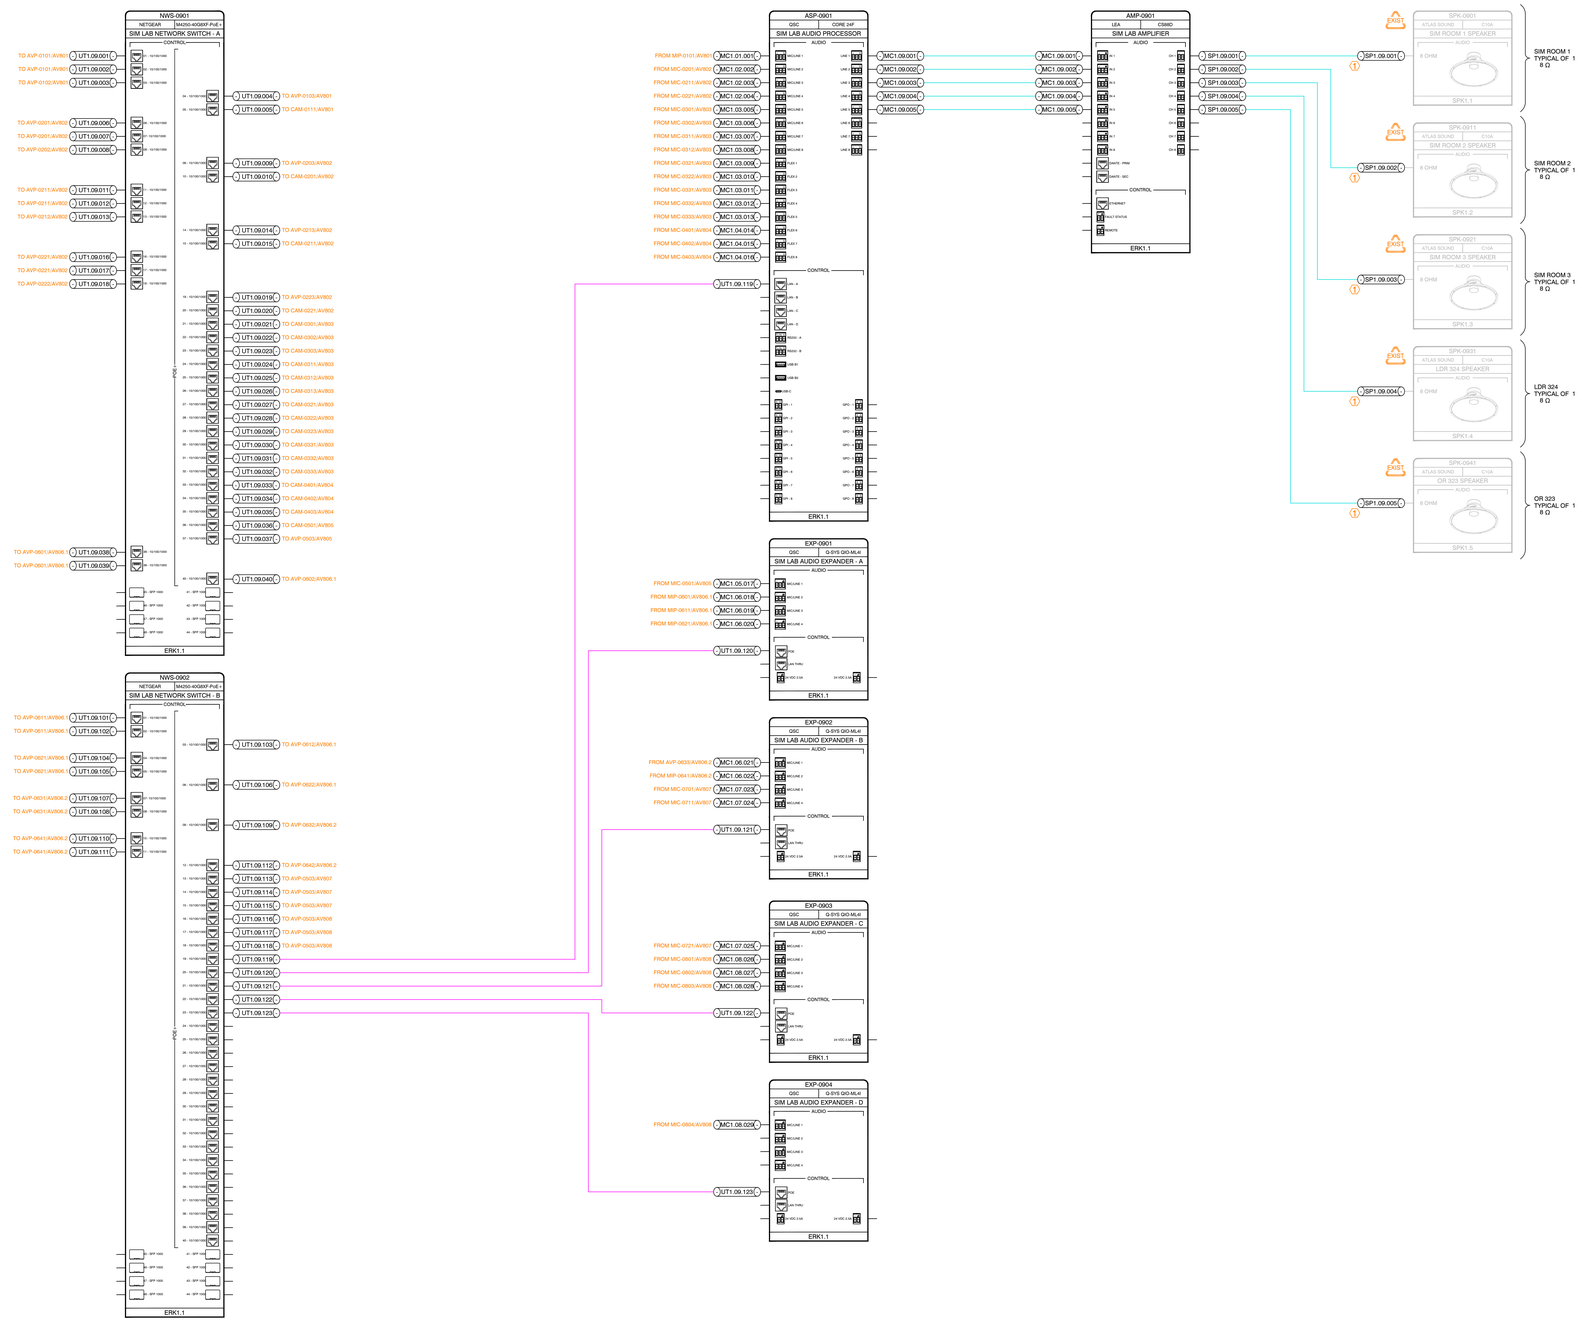

NUM	NOTES
1	REUSE EXISTING CABLE.
2	-
3	-
4	-
5	-
6	-
7	-

LINE DESIGNATIONS KEY

- BULK - AUDIO
- PATCH - AUDIO
- BULK - VIDEO
- PATCH - VIDEO
- BULK - CONTROL
- PATCH - CONTROL
- BULK - EXISTING
- PATCH - EXISTING

MARSHALL INDUSTRIES

www.marshallind.com

PROJECT INFORMATION

6009

LDS HOSPITAL

SIMLAB UPDATE

CUSTOMER NAME: INTERMOUNTAIN HEALTH	CUSTOMER NUMBER: 10340
SITE NAME: LDS HOSPITAL	SITE NUMBER: 122257
SITE ADDRESS: 8TH AVENUE C STREET, SALT LAKE CITY, UT 84143	
SALES PERSON: MATT PRINTY	ENGINEERED BY: MICHAEL PLATTNER
DRAFTER: AARON SMITH	PROJECT MANAGER: DUSTIN DAVIS

DRAWING SET INFORMATION

PHASE: CONSTRUCTION

PUBLISH DATE: 3/17/2026

PLOT SIZE: ARCH FULL BLEED E (36.00 X 48.00 INCHES)

PLOT SCALE: 1' = 1'-0"

APPROVED BY: -----

SHEET REVISION INFORMATION

REVISION: ----

REVISION DATE: -----

REVISION DESCRIPTION: -----

REVISION & ISSUE HISTORY

ISSUED FOR:	REV.	DATE:
---	---	---
---	---	---
LDS HOSPITAL

SINGLE LINE DIAGRAMS

DSP AND SPEAKER ZONES

AV SYSTEM FUNCTIONAL

AV809

FILE NAME: AV800.DWG

ERK-0101

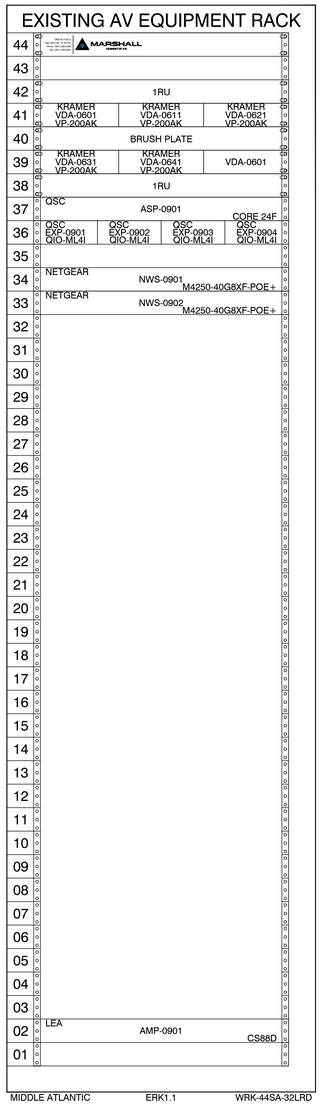

1 **ERK1.1**
SCALE: 3" = 1'-0"

MARSHALL INDUSTRIES

www.marshallind.com

PROJECT INFORMATION

6009

LDS HOSPITAL

SIMLAB UPDATE

CUSTOMER NAME: INTERMOUNTAIN HEALTH	CUSTOMER NUMBER: 10340
SITE NAME: LDS HOSPITAL	SITE NUMBER: 122257
SITE ADDRESS: 8TH AVENUE C STREET SALT LAKE CITY, UT 84143	
SALES PERSON: MATT PRINTY	ENGINEERED BY: MICHAEL PLATTNER
DRAFTER: AARON SMITH	PROJECT MANAGER: DUSTIN DAVIS

DRAWING SET INFORMATION

PHASE: CONSTRUCTION

PUBLISH DATE: 3/17/2026

PLOT SIZE: ARCH FULL BLEED E (36.00 X 48.00 INCHES)

PLOT SCALE: 1' = 1'-0"

APPROVED BY: ----

SHEET REVISION INFORMATION

REVISION:	REVISION DATE:	REVISION DESCRIPTION:
----	----	----

REVISION & ISSUE HISTORY

ISSUED FOR:	REV.	DATE:
---	---	---
---	---	---
LDS HOSPITAL

ENCLOSURE ELEVATIONS

AUDIOVISUAL EQUIPMENT RACK

ERK1.1

AV901

FILE NAME: AV900.DWG